AutoCAD®2004

test 11/08 7.25

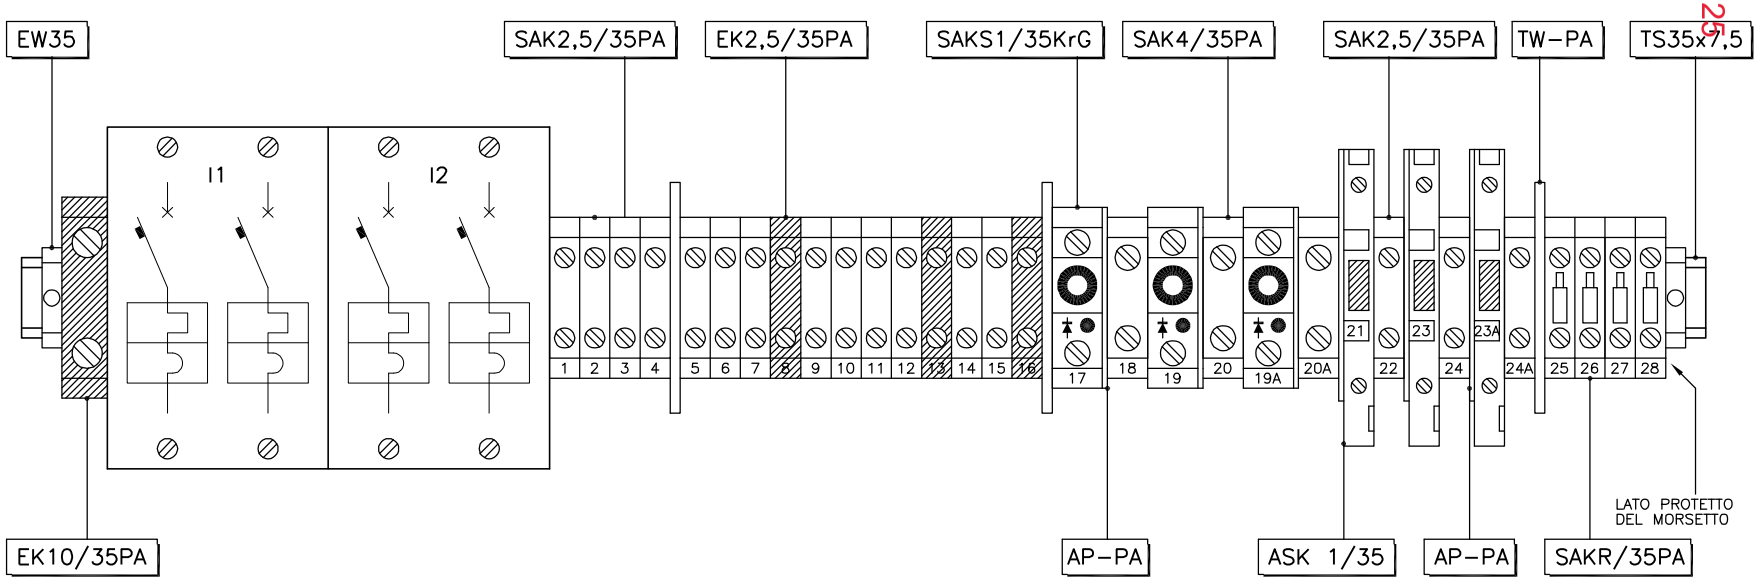

NOTA: PER I MATERIALI FARE RIFERIMENTO ALLA LISTA PARTI L-1217-0012-05

ATTENZIONE: I MORSETTI 17,19 E 19A CON DIODO INDICATORE DEVONO ESSERE MONTATI NEL VERSO INDICATO DAL DISEGNO.

MORSETTIERA ARMADIO CON 3 EMETTITORI

Disegnato da: Vettori Franco	Titolo: ARMADIO UTENTE DI PISTA Composizione morsettiera armadio 3 emettitori.	
Data disegno: 24/11/98		
Approvato da:	Materiale: Peso:	Dis. N° G-1217-0033-98 File: ARMMORS2
Data approv.:		
Rev.: 1 Data: 10/10/05	Trattamenti:	autostrade per l'italia
Documento di proprietà di *Autostrade per l'italia S.p.A.* riprod. vietata a termini di legge	Foglio: 1 di: 1 A3 Scala:	CONCESSIONI E COSTRUZIONI AUTOSTRADE S.p.A.