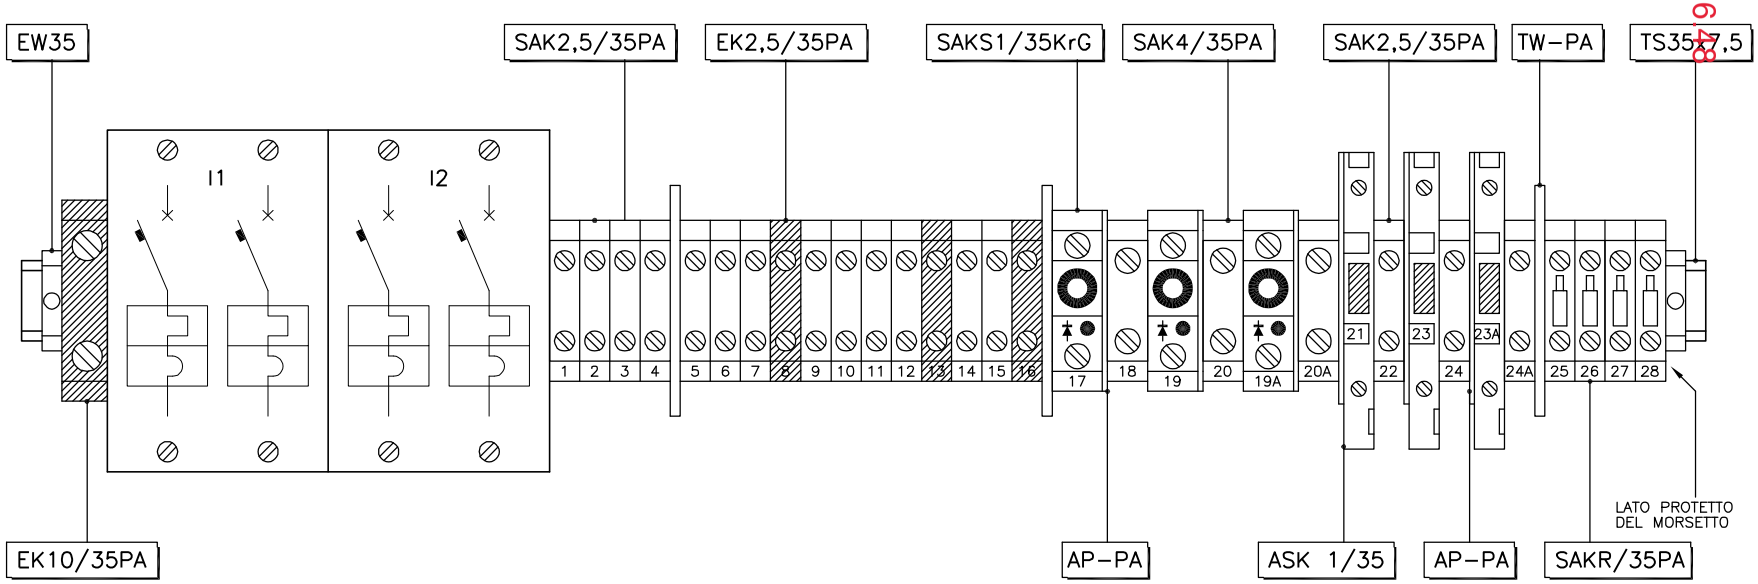

NOTA: PER I MATERIALI FARE RIFERIMENTO ALLA LISTA PARTI L-1217-0012-05

ATTENZIONE: I MORSETTI 17,19 E 19A CON DIODO INDICATORE DEVONO ESSERE MONTATI NEL VERSO INDICATO DAL DISEGNO.

MORSETTIERA ARMADIO CON 3 EMETTITORI

Disegnato da: Vettori Franco	Titolo: ARMADIO UTENTE DI PISTA Composizione morsettiera armadio 3 emettitori.
Data disegno: 24/11/98	
Approvato da:	Materiale:
Data approv.:	Peso:
Rev.: 1 Data: 10/10/05	Trattamenti:
Documento di proprietà di *Autostrade per l'italia S.p.A.* riprod. vietata a termini di legge	Foglio: 1 di: 1 A3 Scala:

Dis. N° G-1217-0033-98
File: ARMMORS2

autostrade per l'italia
CONCESSIONI E COSTRUZIONI AUTOSTRADE S.p.A.

AutoCAD® 2004
test 11/08/25 6:48